



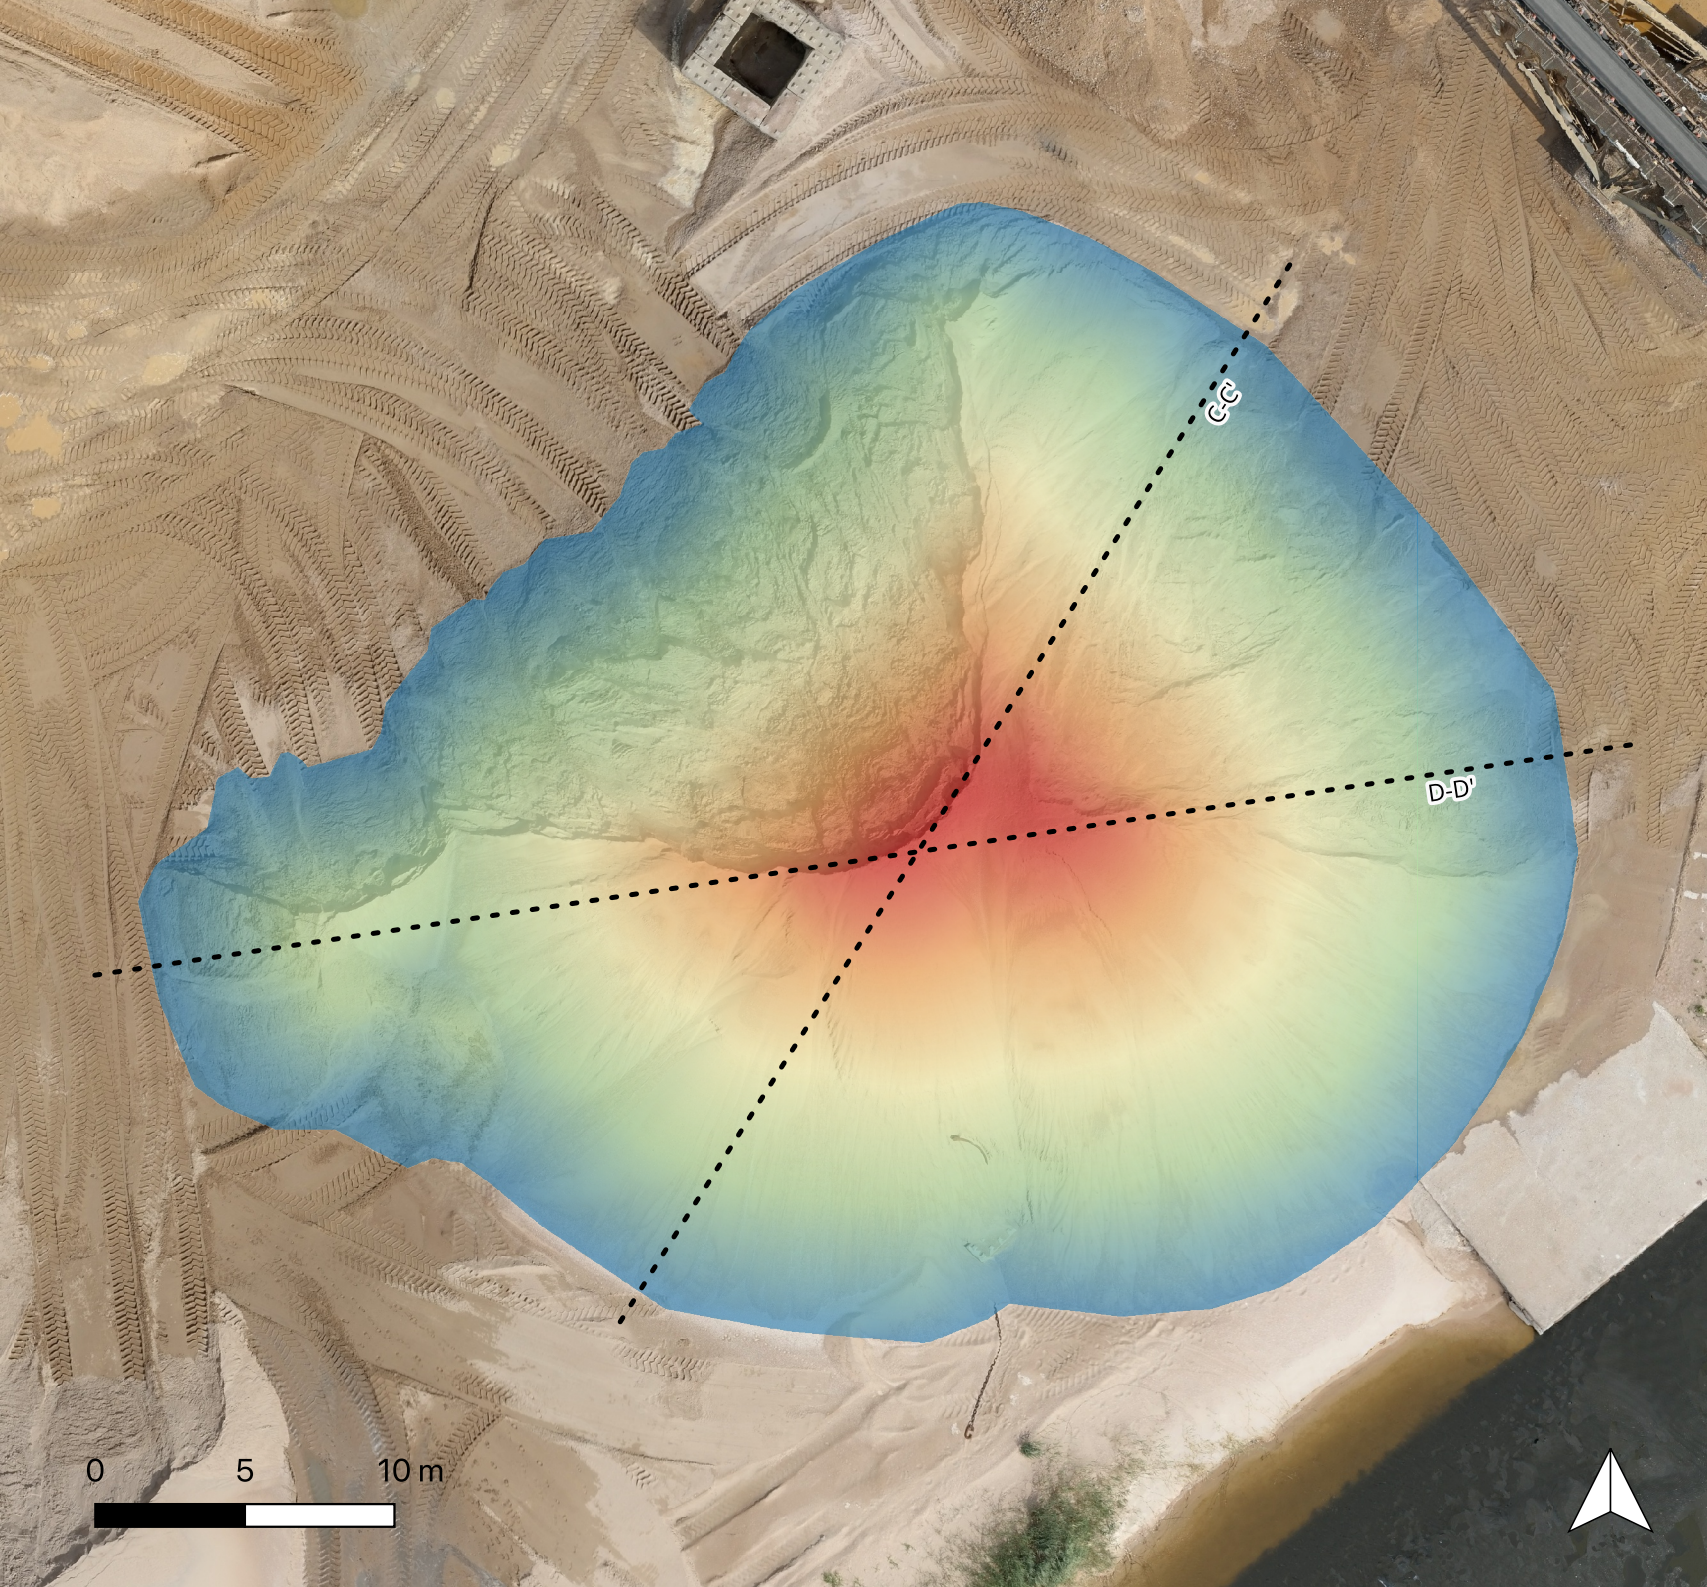

P02 Stockpile Height Above Estimated TIN Base

Zeebrugge aggregate yard — QGIS
volumetric analysis

Height above estimated TIN base (m)

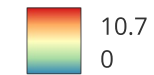

Footprint area 1,207.32 m²

Maximum height 10.74 m

Estimated volume 4,4120.86 m³
5,771.80 yd³

Base surface: cleaned perimeter TIN
generated from 533 reviewed DSM control
points.

Fitted-plane estimate: 4,493.58 m³
(+1.83%)

A short chain/equipment-affected
perimeter interval was excluded from the
TIN controls. Embedded equipment within
the pile footprint was not separately
removed from the DSM.

Demonstration analysis using a public
Virtual Surveyor dataset; not a certified
survey deliverable.